


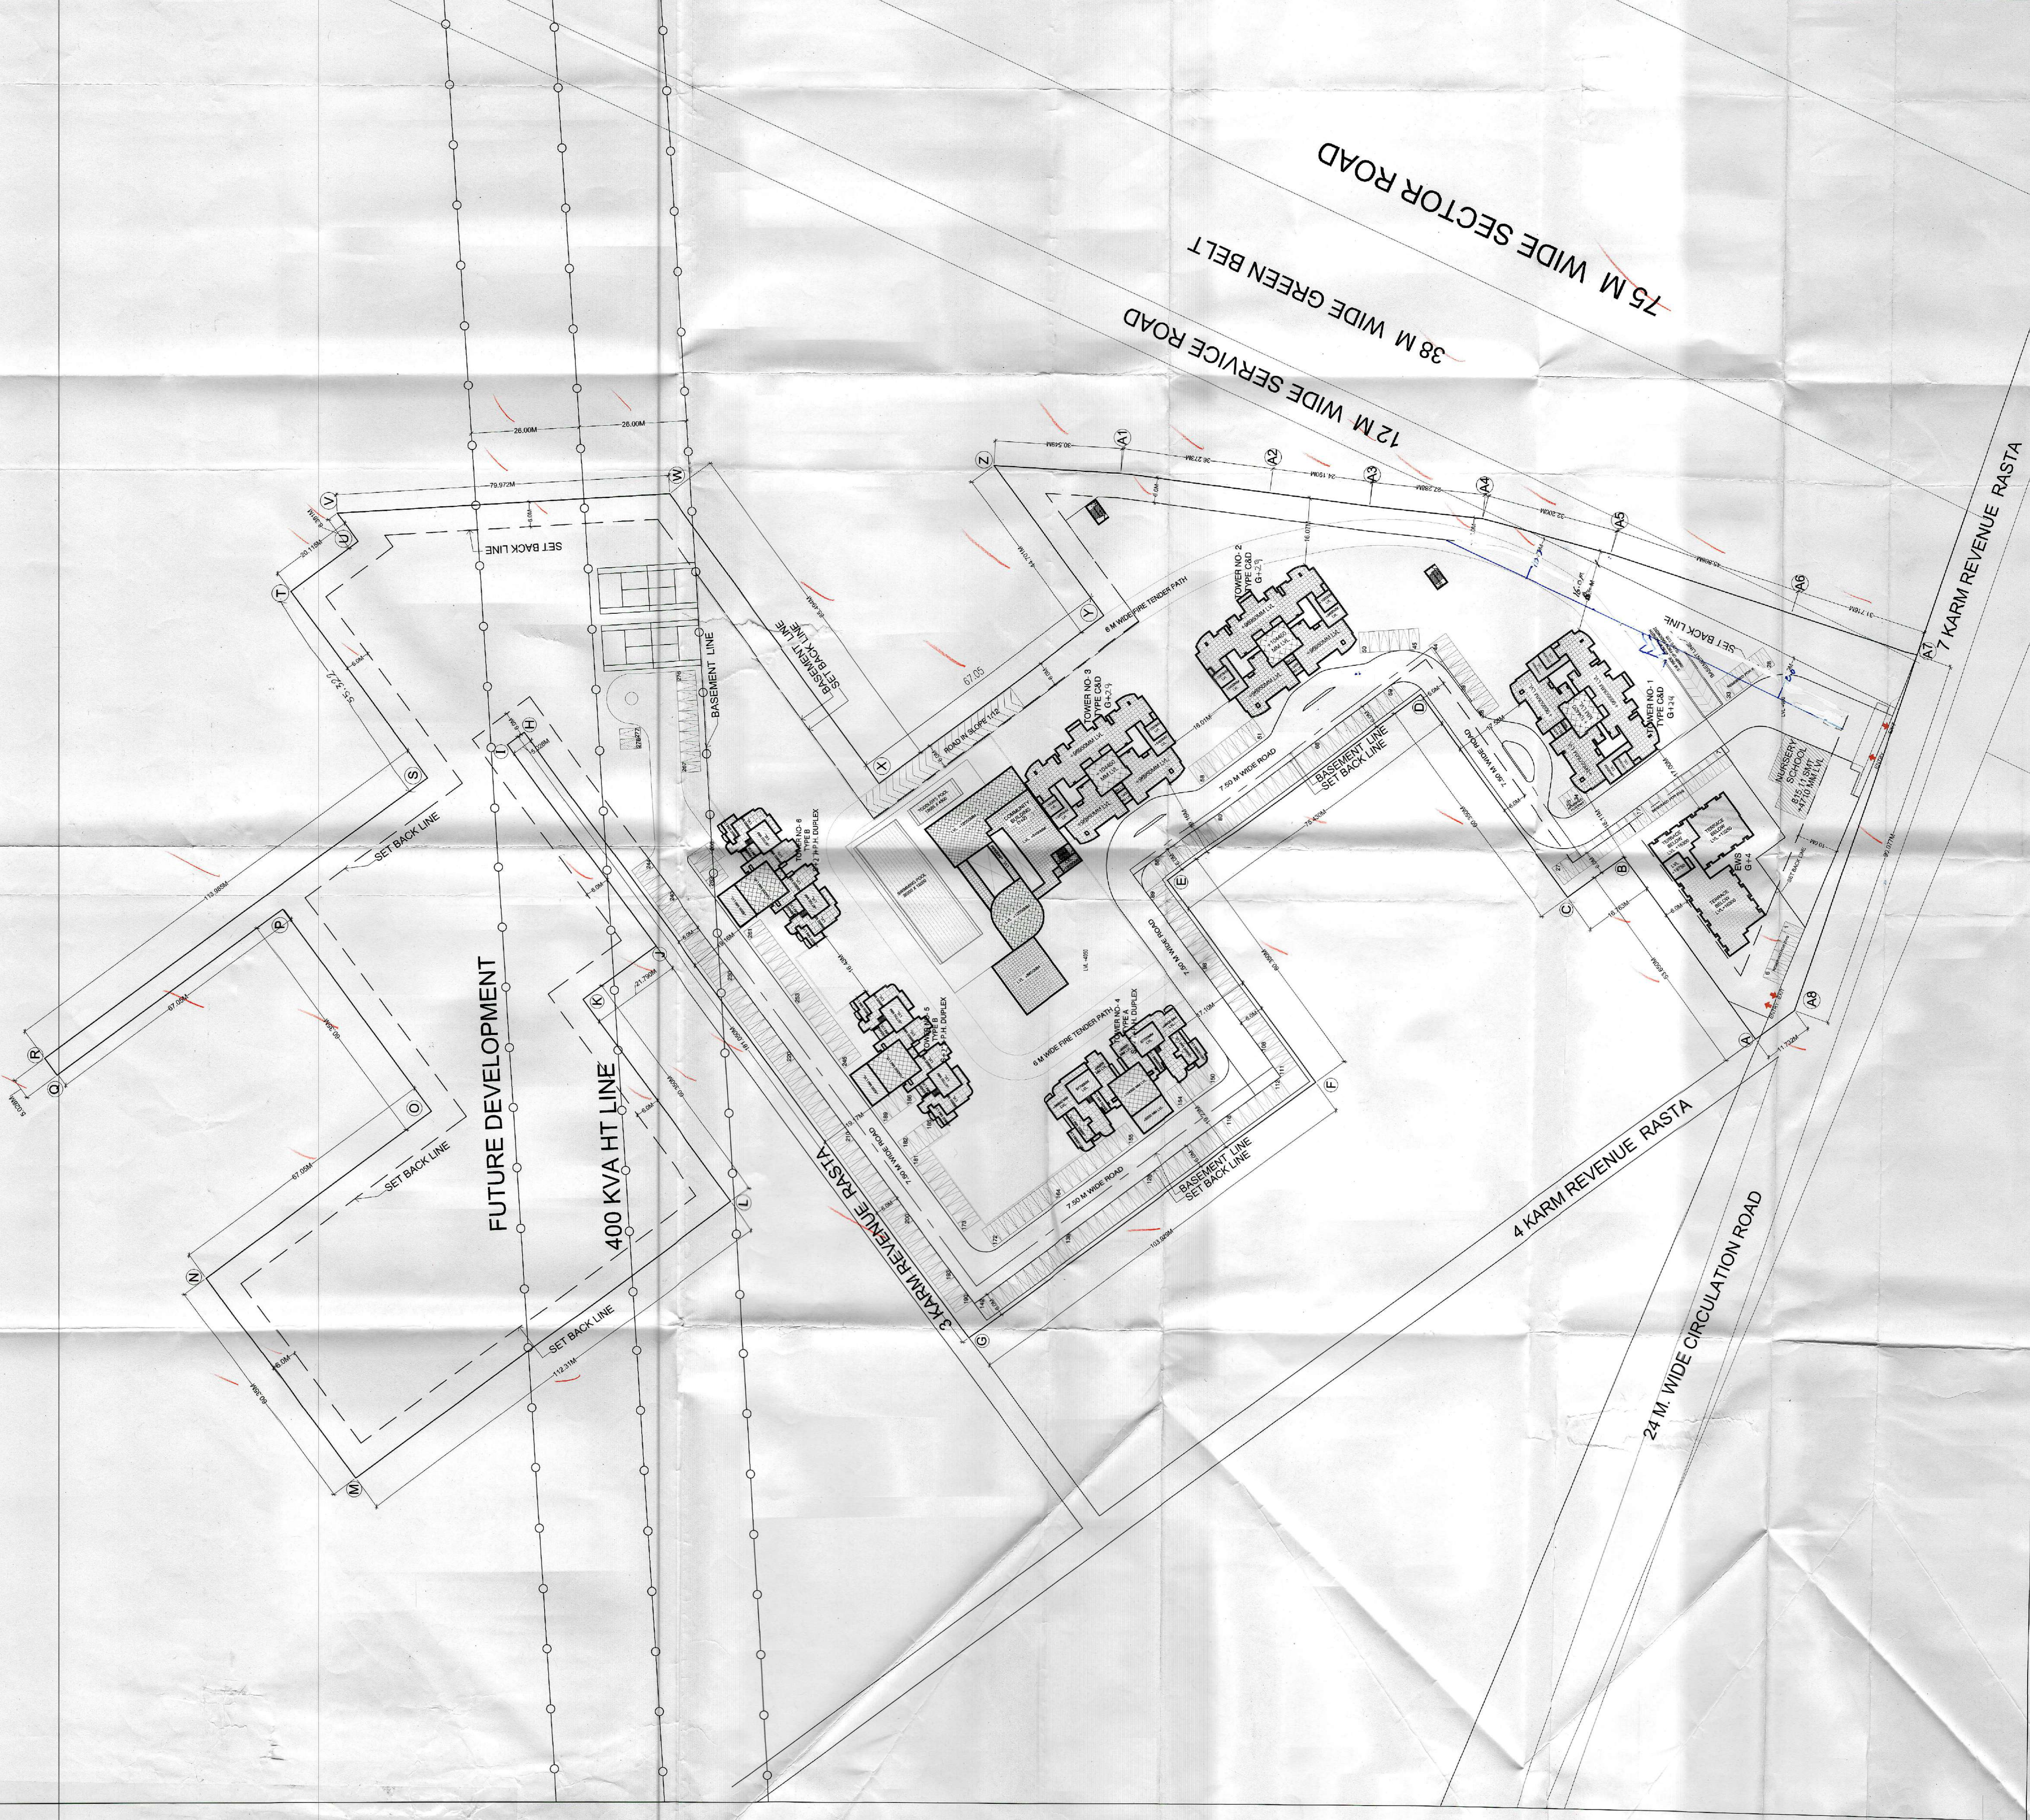

| ABSTRACT                  |               |
|---------------------------|---------------|
| TOTAL SITE AREA           | 11.5075 Acres |
| SITE AREA (As Calculated) | 46528.66 sqm  |
| 24hr Permitted GFA        | 20,321 sqm    |
|                           | 81425.15 sqm  |

| DETAILS OF MAIN D.U.'S PROPOSED |                    |                    |                |                |
|---------------------------------|--------------------|--------------------|----------------|----------------|
| TOWER-1 TYPE-C & D              | TOWER-2 TYPE-C & D | TOWER-3 TYPE-C & D | TOWER-4 TYPE-A | TOWER-5 TYPE-B |
| No. of D.U. per TOWER           | 118                | 118                | 118            | 56             |
| Total                           | 118                | 118                | 118            | 56             |
| Total Main D.U.S                |                    |                    |                |                |
| 522                             |                    |                    |                |                |

| PROPOSED POPULATION             |              |
|---------------------------------|--------------|
| Population of Main Units        | 2600 persons |
| Population of Service Personnel | 100 persons  |
| Population of EWS Units         | 150 persons  |
| Population of EWS Units         | 150 persons  |
| TOTAL POPULATION                | 2800 persons |

| PARAMETERS                                |                              |
|-------------------------------------------|------------------------------|
| PARAMETER                                 | PERMISSIBLE                  |
| Ground Coverage                           | 35.0% = 16255.03 sqm         |
| F.A.R.                                    | 175 = 81425.15 sqm           |
| No. of Main Units                         | 522 nos.                     |
| No. of EWS units                          | 150 nos.                     |
| TOTAL UNITS                               | 672 nos.                     |
| No. of Service Personnel                  | 100 nos.                     |
| Population                                | 2800 nos.                    |
| Organised Greens                          | 15% = 6979.3                 |
| Convenient Shopping                       | (0.5% of Site Area) = 232.64 |
| Car Parking                               | 1.5 per Main D.U. = 783 nos. |
| Covered Car Parking 75% of Total Required | 587 nos.                     |

| F.A.R. AREA STATEMENT |                        | TOWER-1 |        |        |        |        | TOWER-2 |        |        |        |        | TOWER-3 |        |        |        |        | TOWER-4 |        |        |        |        | TOWER-5 |        |        |        |        | TOWER-6 |        |        |        |        | TOWER-7 |        |        |        |        | EWS    |        |        |        |        | Community Building |        |        |        |        | Convenient Shopping |        |        |        |        | Gate Guard house | |
|---|
| BUILDING DESCRIPTION  |                        | TOWER-1 |        |        |        |        | TOWER-2 |        |        |        |        | TOWER-3 |        |        |        |        | TOWER-4 |        |        |        |        | TOWER-5 |        |        |        |        | TOWER-6 |        |        |        |        | TOWER-7 |        |        |        |        | EWS    |        |        |        |        | Community Building |        |        |        |        | Convenient Shopping |        |        |        |        | Gate Guard house | |
| F.A.R. AREA           | Ground Floor/5th Floor | 402.09  | 402.09 | 4 |